
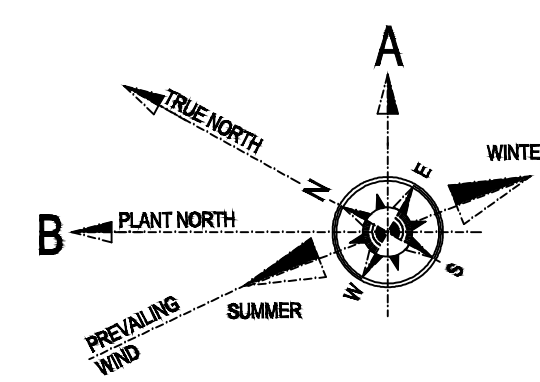


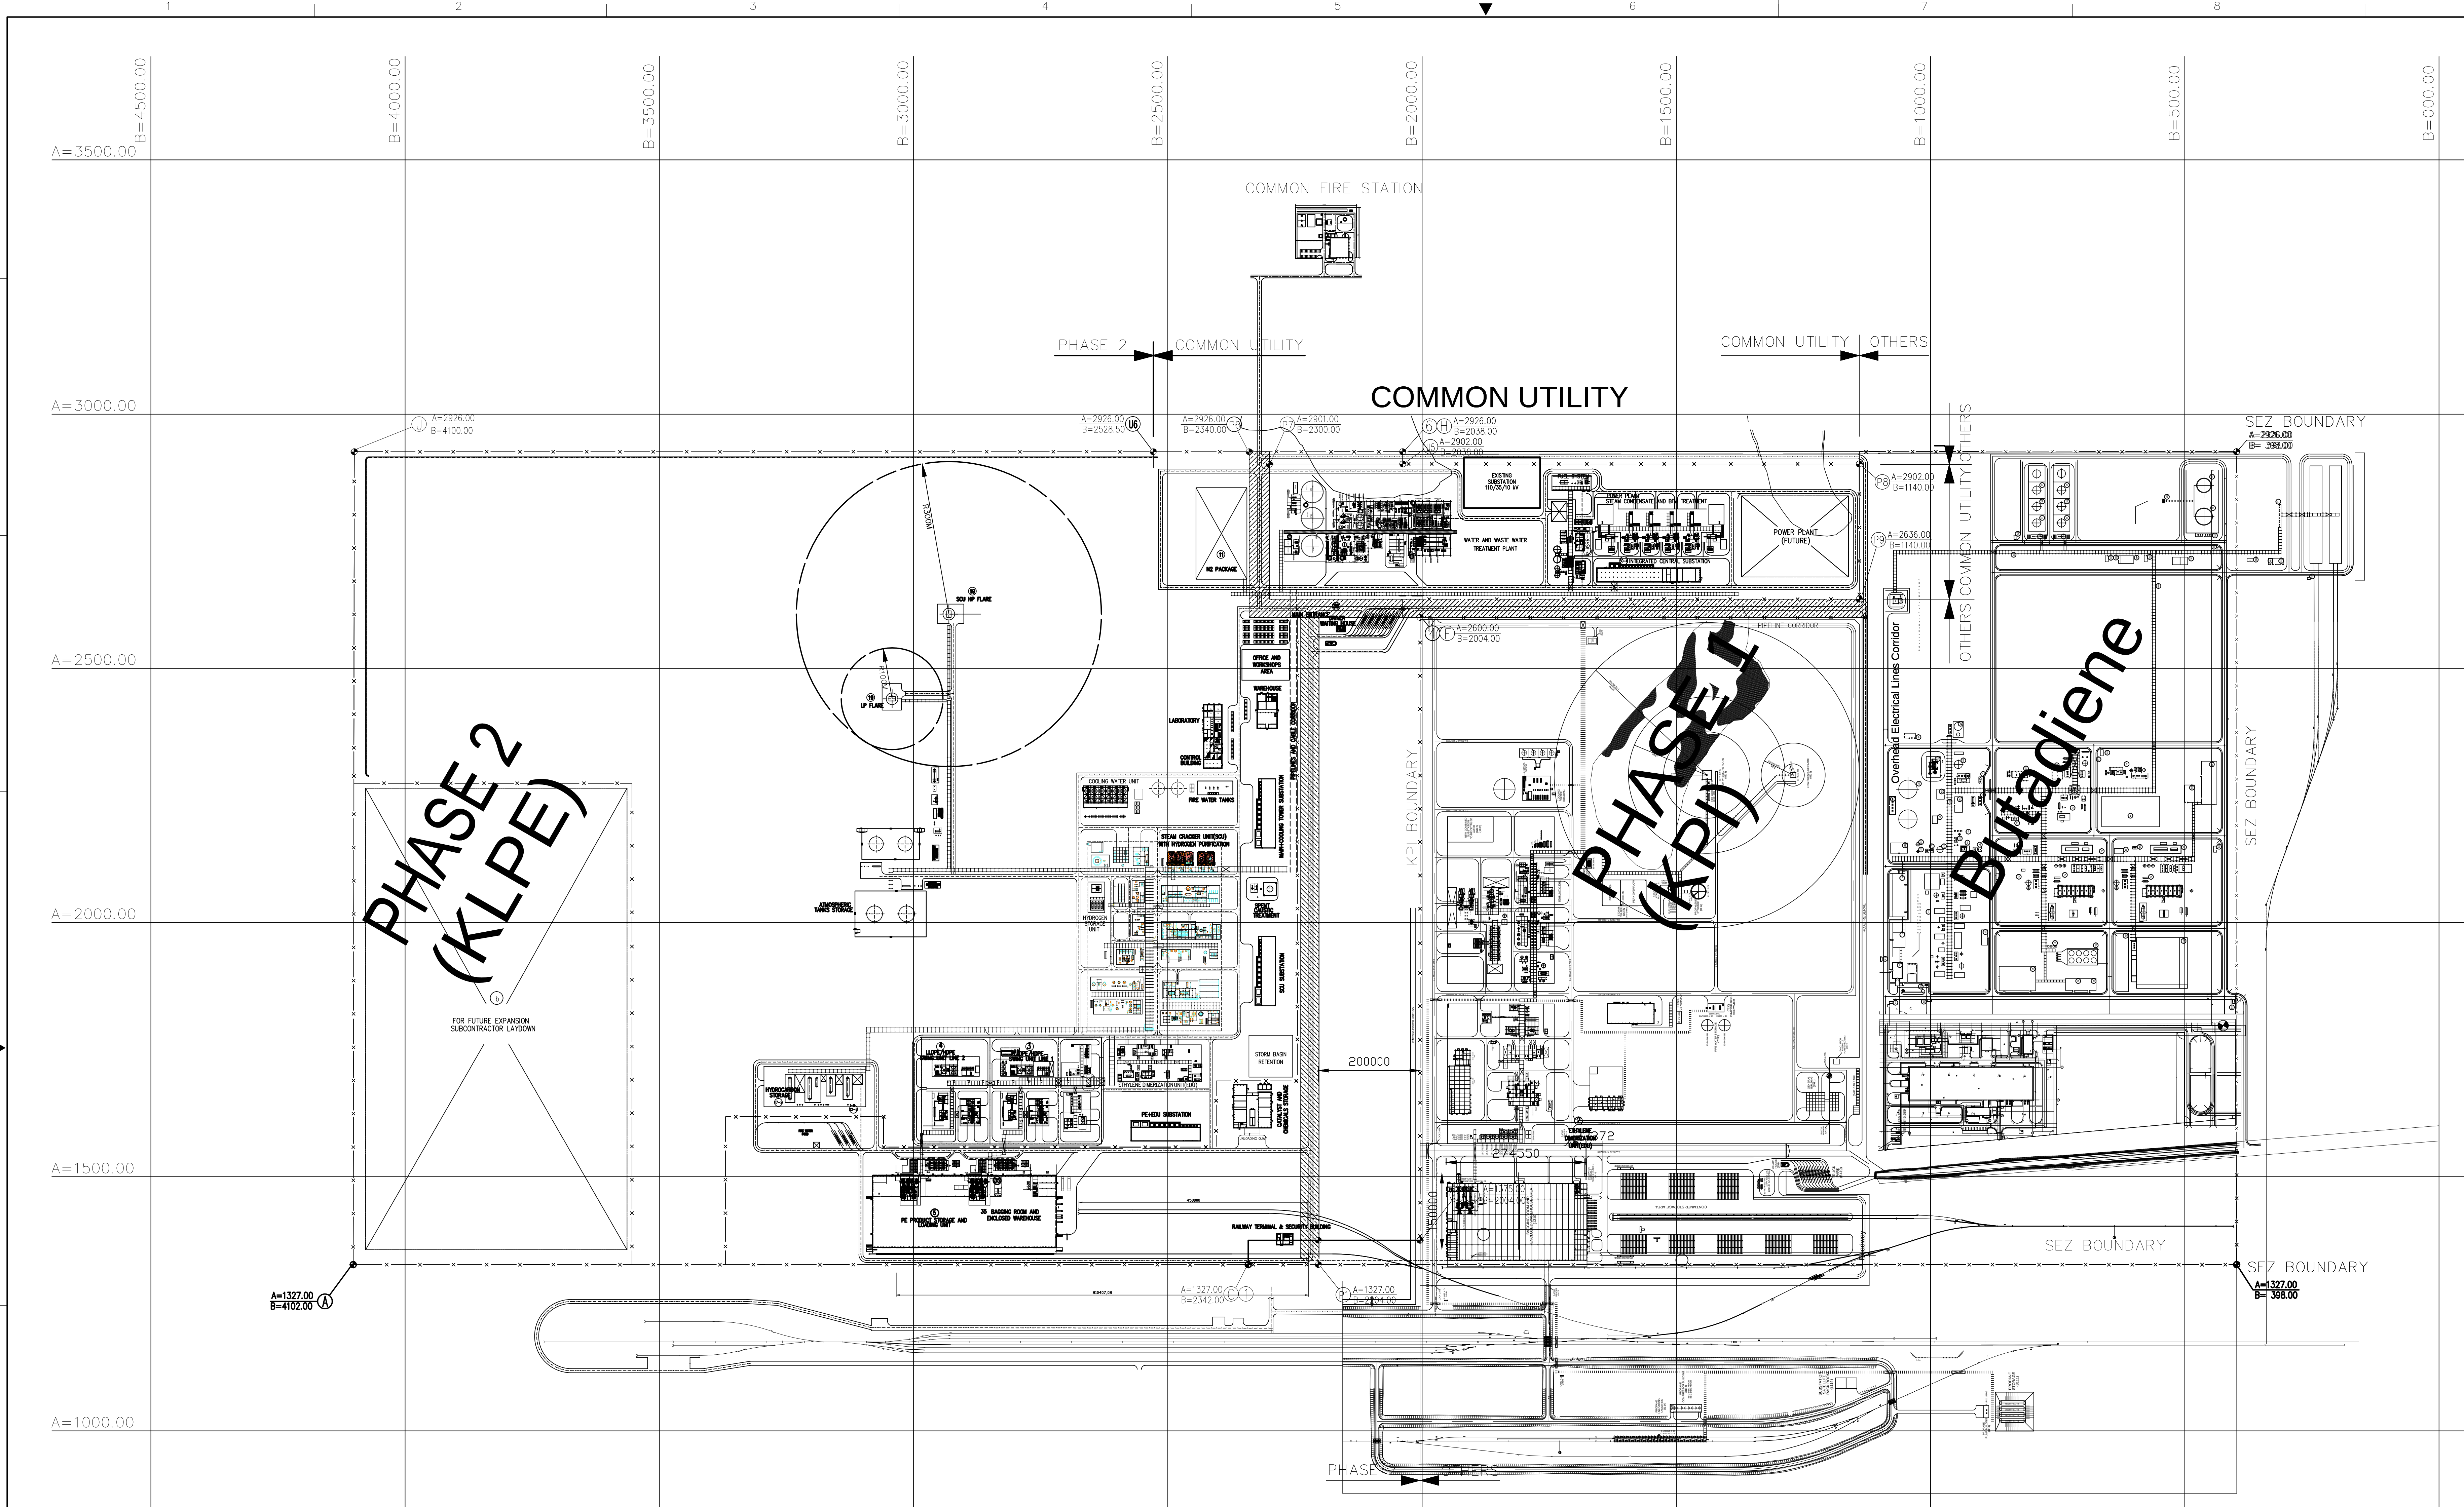


NOTES

1. B AXIS IS AT +30.000648° WITH RESPECT TO TRUE NORTH AXIS.
2. PLANT NORTH AXIS IS AT +30.000648° WITH RESPECT TO TRUE NORTH.
3. THE CONVERSION EQUATION BETWEEN THE A/B COORDINATE SYSTEM AND THE N/E COORDINATE SYSTEM SHALL BE:
N=524.9629 402
E=954.9048 890
G=30.000648
B=(N-N0)COS(G)-(E-E0)SIN(G)
A=(E-E0)COS(G)+(N-N0)SIN(G)
N=60250.00+KINGDOM
E=40250.00+BRAND
4. THE DESIGN ELEVATION OF THE HIGH POINT OF PAVEMENT SHALL BE 22.10M.
5. THE EL100.000 OF THE PLANT VERTICAL DATUM (PVD) SHALL BE THE HIGH POINT OF PAVEMENT (HPP) AND EQUIVALENT TO 22.10M (PVD DATUM).
6. THE UNIT OF ELEVATION IS METER.

LEGEND:

- FENCE PHASE 2
- SEZ BOUNDARY
- COMMON UTILITY AREA FOR PHASE 2 & 1,3
- SSR SATELLITE RACK ROOM
- SSR ELECTRICAL SUBSTATION

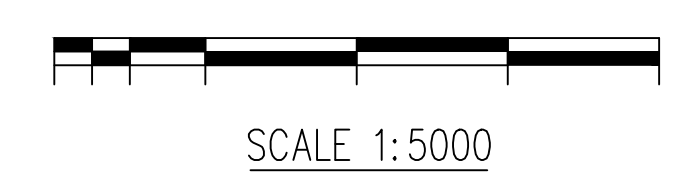

PHASE 2 AREA UNIT LIST

UNIT NO.	ITEM NO.	DESCRIPTION	REFERENCE DRAWING NO.	REMARK	UNIT NO.	ITEM NO.	DESCRIPTION	REFERENCE DRAWING NO.	REMARK
U-2110		STEAM CRACKER UNIT(SOU)	IP02-LE-8230-01-2110-0001		U-2340	30-2	BUILDING AREA SUBSTATION	IP02-OS-8310-47-2340-0001	
U-2110-1	1-1	HYDROGEN STORAGE UNIT	IP02-LE-8230-01-2110-0001			30-3	COOLING TOWER SUBSTATION	IP02-OS-8310-47-2340-0001	
U-2120	2	ETHYLENE IMERIZATION UNIT(EIU)	IP02-OS-8310-01-2120-0001			30-4	U&O SUBSTATION	IP02-OS-8310-47-2340-0001	
U-2130	3	LLDPE/HDPE SWING UNIT LINE 1	IP02-OS-8310-01-2130-0001			30-5	COMMON VMD SUBSTATION	IP02-OS-8310-47-2340-0001	
U-2131	4	LLDPE/HDPE SWING UNIT LINE 2	IP02-OS-8310-01-2130-0001			30-6	INTEGRATED CENTRAL SUBSTATION	IP02-OS-8310-47-2340-0001	
U-2132	5	PE PRODUCT STORAGE AND LOADING UNIT	IP02-OS-8310-01-2132-8601			30-7	WMT SUBSTATION	IP02-OS-8310-47-2340-0001	
U-2140	1	HYDROGEN PURIFICATION UNIT	IP02-LE-8230-01-2110-0001			32-1	SATELLITE RACK ROOM -1 IN MAIN SUBSTATION UNIT	IP02-OS-8310-47-2340-0108	
U-2200	30-1	MAIN SUBSTATION (PE+EDU+MAN)	IP02-OS-8310-47-2340-0001			32-2	SATELLITE RACK ROOM -4 IN HYDROCARBON STORAGE UNIT	IP02-OS-8310-47-2340-0108	
U-2210	6	POWER PLANT	IP02-OS-8310-01-2210-0001			32-3	SATELLITE RACK ROOM -5 IN DEMINERALISED WATER UNIT	IP02-OS-8310-47-2340-0108	
U-2211	7	WATER TREATMENT PLANT	IP02-OS-8310-01-2211-0001	With item 14, 15, 16		32-4	SATELLITE RACK ROOM -6 IN POWER PLANT UNIT	IP02-OS-8310-47-2340-0108	
U-2212	8	STEAM CONDENSATE AND BFW TREATMENT	IP02-OS-8310-01-2212-0001		32-5	SATELLITE RACK ROOM -7 IN WASTE WATER TREATMENT UNIT	IP02-OS-8310-47-2340-0108		
U-2221	9	COOLING WATER UNIT	IP02-OS-8310-01-2221-0001		33	RAILWAY TERMINAL & SECURITY BUILDING	IP02-OS-8310-47-2340-0501		
U-2222	10	FUEL SYSTEM	IP02-OS-8310-01-2222-0001		34	WASTE STORAGE BUILDING	IP02-OS-8310-47-2340-1301		
U-2223	21	HOT WATER SYSTEM	IP02-OS-8310-01-2223-0001		35	BAGGING ROOM AND ENCLOSED WAREHOUSE	IP02-OS-8310-47-2340-0302		
U-2224	11	NITROGEN PLANT	IP02-OS-8310-01-2224-0001		18	CATALYST AND CHEMICALS STORAGE	IP02-OS-8310-47-2350-0401		
U-2225	12	PLANT AIR AND INSTRUMENT AIR UNIT	IP02-OS-8310-01-2224-0001		23	FIRE FIGHTING BUILDING UNIT	IP02-OS-8310-47-2350-0102		
U-2226	13	SPENT CAUSTIC TREATMENT UNIT	IP02-OS-8310-01-2226-0001		25	ADMINISTRATION BUILDING	IP02-OS-8310-47-2350-0002		
U-2230	14	RAW WATER STORAGE	IP02-OS-8310-01-2221-0001	Included in Item 7	29	WORKSHOP	IP02-OS-8310-47-2350-0602		
U-2231	15	SERVICE WATER STORAGE	IP02-OS-8310-01-2211-0001	Included in Item 7	37-1	MAIN GUARD HOUSE	IP02-OS-8310-47-2350-1601		
U-2232	16	POTABLE WATER STORAGE	IP02-OS-8310-01-2211-0001	Included in Item 7	37-2	LOGISTICS GUARD HOUSE	IP02-OS-8310-47-2350-1601		
U-2233	8	DEMINERALISED WATER UNIT	IP02-OS-8310-01-2233-0001		37-3	GUARD HOUSE	IP02-OS-8310-47-2350-1601		
U-2241	22	THERMAL OXIDIZER UNIT	IP02-OS-8310-01-2241-0001		38	WMT OFFICE BUILDING	IP02-OS-8310-47-2350-2001		
U-2310	17-1	ATMOSPHERIC TANKS STORAGE	IP02-OS-8310-01-2310-0001		39	DRIVERS WAITING HOUSE	IP02-OS-8310-47-2350-0901		
U-2310	17-2	HYDROCARBON STORAGE	IP02-OS-8310-01-2310-0001		U-2360	a	AREA FOR FUTURE ADDITIONAL LLPE TRAIN	N/A	For future
U-2320	19	FLARE UNIT(2 HP FLARE, 1 LP FLARE)	IP02-OS-8310-01-2320-0001			b	FOR FUTURE EXPANSION SUBCONTRACTOR LAYOUT	N/A	For future
U-2330	20	WASTE WATER TREATMENT	IP02-OS-8310-01-2330-0001			c	FOR FUTURE EXPANSION SUBCONTRACTOR'S OFFICES	N/A	For future
U-2340	24	CONTROL CENTER BUILDING	IP02-OS-8310-47-2350-0002			d	AREA FOR FUTURE ADDITIONAL FURNACE	N/A	For future
	31	COMMON UTILITY CONTROL BUILDING	IP02-OS-8310-47-2350-1701						
	27	LABORATORY BUILDING	IP02-OS-8310-47-2350-0302						
	28	WAREHOUSE	IP02-OS-8310-47-2350-0502						

COMMON UTILITY AREA UNIT LIST

ITEM	UNIT NO.	DESCRIPTION	W	L	REMARK
6	U-2210	POWER PLANT			
7	U-2233	DEMINERALISED WATER UNIT			
8	U-2211	WATER TREATMENT PLANT			With item 14, 15, 16
10	U-2222	FUEL SYSTEM			
11	U-2224	NITROGEN PLANT			
12	U-2225	PLANT AIR AND INSTRUMENT AIR UNIT			
14	U-2230	RAW WATER STORAGE			Included in item 7
15	U-2231	SERVICE WATER STORAGE			Included in item 7
16	U-2232	POTABLE WATER STORAGE			Included in item 7
20	U-2330	WASTE WATER TREATMENT			

COORDINATES OF PHASE 2(KLPE PROJECT)

MARK	E(X)	N(Y)	Lot	U(m)	A	B
A	9544147.220	5247845.090	47° 21' 27.68966"	52° 14' 41.67556"	1327.00	4102.00
B, 11	9544549.350	5247148.830	47° 21' 04.94119"	52° 15' 00.30123"	1327.00	3298.00
C, 1	9550227.075	5246321.133	47° 20' 37.89748"	52° 15' 22.42212"	1327.00	2342.00
D, 2	9550208.443	5246345.133	47° 20' 38.65270"	52° 15' 24.42039"	1375.00	2342.00
E, 3	9552337.620	5246052.450	47° 20' 29.08939"	52° 15' 32.24332"	1375.00	2004.00
F, 4	9550208.521	5246664.930	47° 20' 48.39899"	52° 16' 23.24669"	2600.00	2004.00
G, 5	9556281.520	5246694.375	47° 20' 49.32120"	52° 16' 22.45983"	2600.00	2038.00
H, 6	9556564.203	5246857.586	47° 20' 54.45503"	52° 16' 36.05174"	2926.00	2038.00
I, 12	9555354.680	5247846.630	47° 21' 30.24365"	52° 16' 06.91121"	2926.00	3298.00
J	9555332.670	5248643.320	47° 21' 52.79810"	52° 15' 48.29647"	2926.00	4100.00
P1					2402.00	2204.00
P2					2402.00	2204.00
P3					2402.00	2204.00
P4					2596.00	2024.00
P5					2596.00	2340.00
P6					2926.00	2340.00
P7					2902.00	2300.00
P8					2902.00	1140.00
P9					2636.00	1140.00
P10					2636.00	2300.00

Coordinate conversion of selected elements from: Krassovsky 1940 Gauss Kruger (UTM-40-1) to: WGS84 Geographic

COORDINATES OF PHASE 2(KLPE)

MARK	A(PLANT EAST)	B(PLANT NORTH)
J	2926.00	4100.00
A	1327.00	4102.00
C, 1	1327.00	2342.00
D, 2	1375.00	2342.00
3, E	1375.00	2004.00
4, F	2600.00	2004.00
5, G	2600.00	2038.00
U	2636.00	2038.00
P8	2636.00	1140.00
P9	2902.00	1140.00
6, H	2926.00	2038.00
U	2926.00	2038.00

COORDINATES OF COMMON UTILITY AREA

MARK	A(PLANT EAST)	B(PLANT NORTH)
U1	2305.20	2528.50
U2	2305.20	2204.00
P2	2402.00	2204.00
U3	2402.00	2004.00
4, F	2600.00	2004.00
5, G	2600.00	2038.00
U4	2636.00	2038.00
P9	2636.00	1140.00
P8	2902.00	1140.00
U5	2902.00	2038.00
6, H	2926.00	2038.00
U6	2926.00	2528.50

APPROVAL CODES		DESCRIPTION								
☐	1	APPROVED								
☐	2	APPROVED WITH COMMENTS. CONTRACTOR CAN PROCEED, REVISE, AND RESUBMIT INCORPORATING THE COMMENTS.								
☐	3	REVIEWED AND RETURNED WITH COMMENTS. DO NOT PROCEED INCORPORATE COMMENTS AND RESUBMIT.								
☐	4	INFORMATION ONLY								
NAME		DATE								
SIGN		SIGN								
REV	DATE	DESCRIPTION	BY	CHKD	LEAD	ENG	PROJ	APPD	CHN	APPD
CLIENT PROJECT NO: IPCI-2										
INTEGRATED PETROCHEMICAL COMPLEX AND INFRASTRUCTURE PROJECT PHASE-2										
DRAWING TITLE										
ELECTRONIC FILE :										
CONTRACT ORIGINATOR DISC. TYPE UNIT SERIAL NO. REV										
DWG.:										